



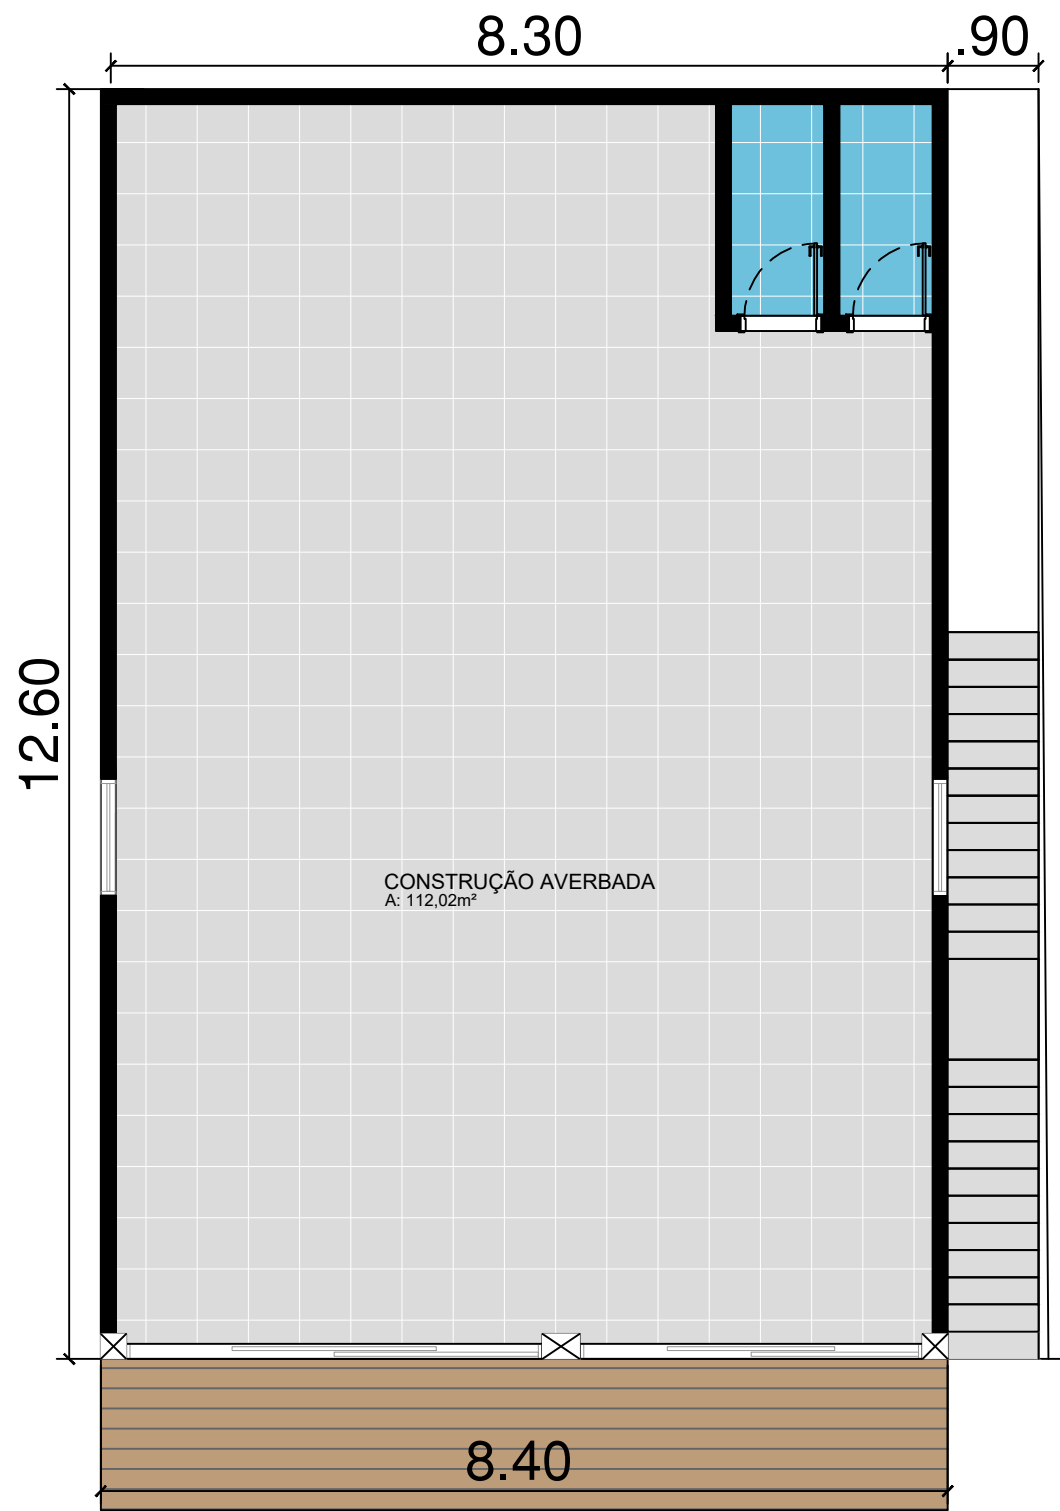

PLANTA PAVIMENTO TÉRREO

esc 1:75

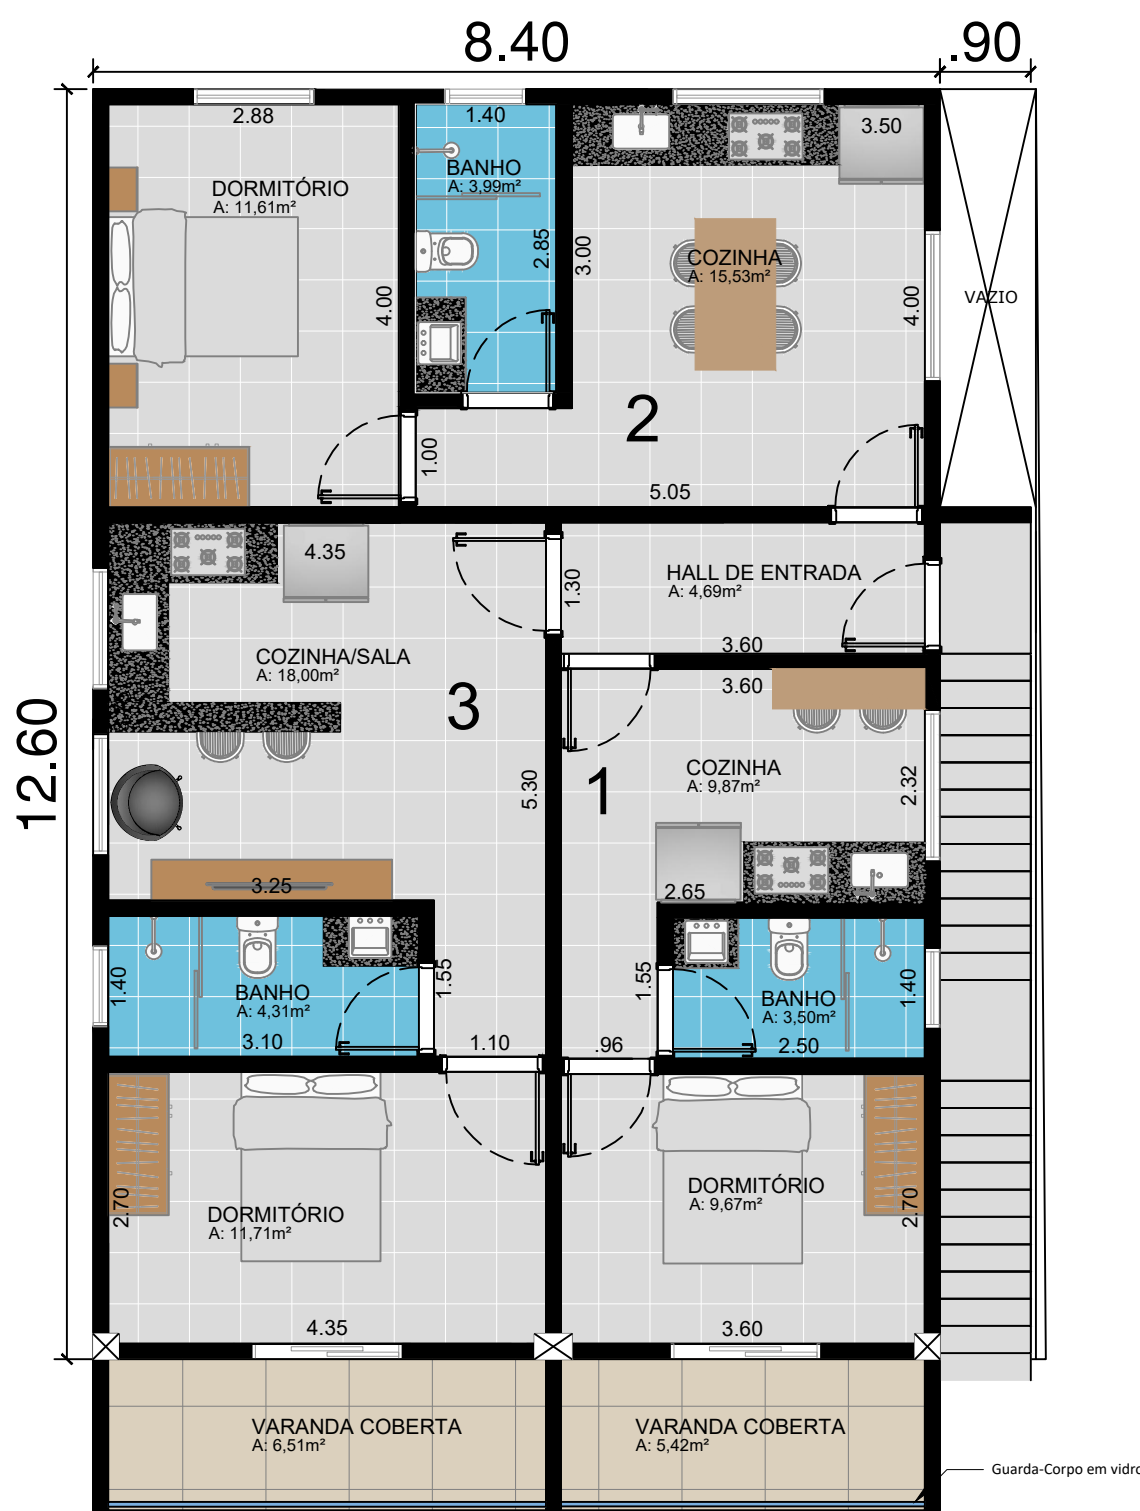

PLANTA PAVIMENTO SUPERIOR

esc 1:75

NOTAS GERAIS

- 1 - ESTE PROJETO É PROPRIEDADE DO PROJETISTA REGISTRADO NO SELO. CONFORME LEI N°: 5194/66 NÃO DEVE SER UTILIZADO PARA QUALQUER OUTRA FINALIDADE QUE NÃO SE RELACIONE COM A EXECUÇÃO DA PRESENTE EDIFICAÇÃO, SENDO TERMINANTEMENTE VEDADA SUA COLOCAÇÃO A DISPOSIÇÃO DE TERCEIROS.
- 2 - O PROJETISTA NÃO SE RESPONSABILIZARÁ POR EVENTUAIS ALTERAÇÕES DESTES PROJETO DURANTE SUA EXECUÇÃO. QUALQUER MODIFICAÇÃO, O MESMO DEVE SER CONTACTADO.
- 3 - ESTE PROJETO FOI BASEADO NO LAY-OUT E INFORMAÇÕES FORNECIDAS PELO ARQUITETO OU PROPRIETÁRIO.
- 4 - QUALQUER MODIFICAÇÃO OU DÚVIDA DEVERÁ SER IMEDIATAMENTE COMUNICADA POR ESCRITO AO PROJETISTA.

PROJETO ARQUITETÔNICO

Folha  
1/1

Objetivo: Projeto de Construção de Residência Unifamiliar

Proprietário(s): Donato Cenciani e Rosana Cenciani

Local: Praça Nossa Senhora Aparecida - BR° Centro

Município(s): Pedra Bela

Estado UF: SP

Matricula: 2136900240/62

Zoneamento: Área Urbana - AU

Escala: Indicada

Data: Março 2026

SITUAÇÃO: SEM ESCALA



DECLARO QUE A APROVAÇÃO DESTES PROJETO NÃO IMPLICA NO RECONHECIMENTO POR PARTE DA PREFEITURA DO DIREITO DE PROPRIEDADE DO TERRENO.

A INSTALAÇÃO E CONSERVAÇÃO DOS RESERVATÓRIOS DE ÁGUA ATENDERÃO AO DISPOSTO NOS ARTIGOS 10 E 11 DO DECRETO N° 12.342/78

PROPRIETÁRIO:  
DONATO CENCIANI

PROPRIETÁRIA:  
ROSANA CENCIANI

RESPONSÁVEL TÉCNICO:

L.C. ENGENHARIA E ARQUITETURA LTDA  
CNPJ: 53.365.242/0001-45  
Lucas Gabriel De Souza  
Engenheiro Civil  
CREA/SP: 5069815955

APROVAÇÕES: